
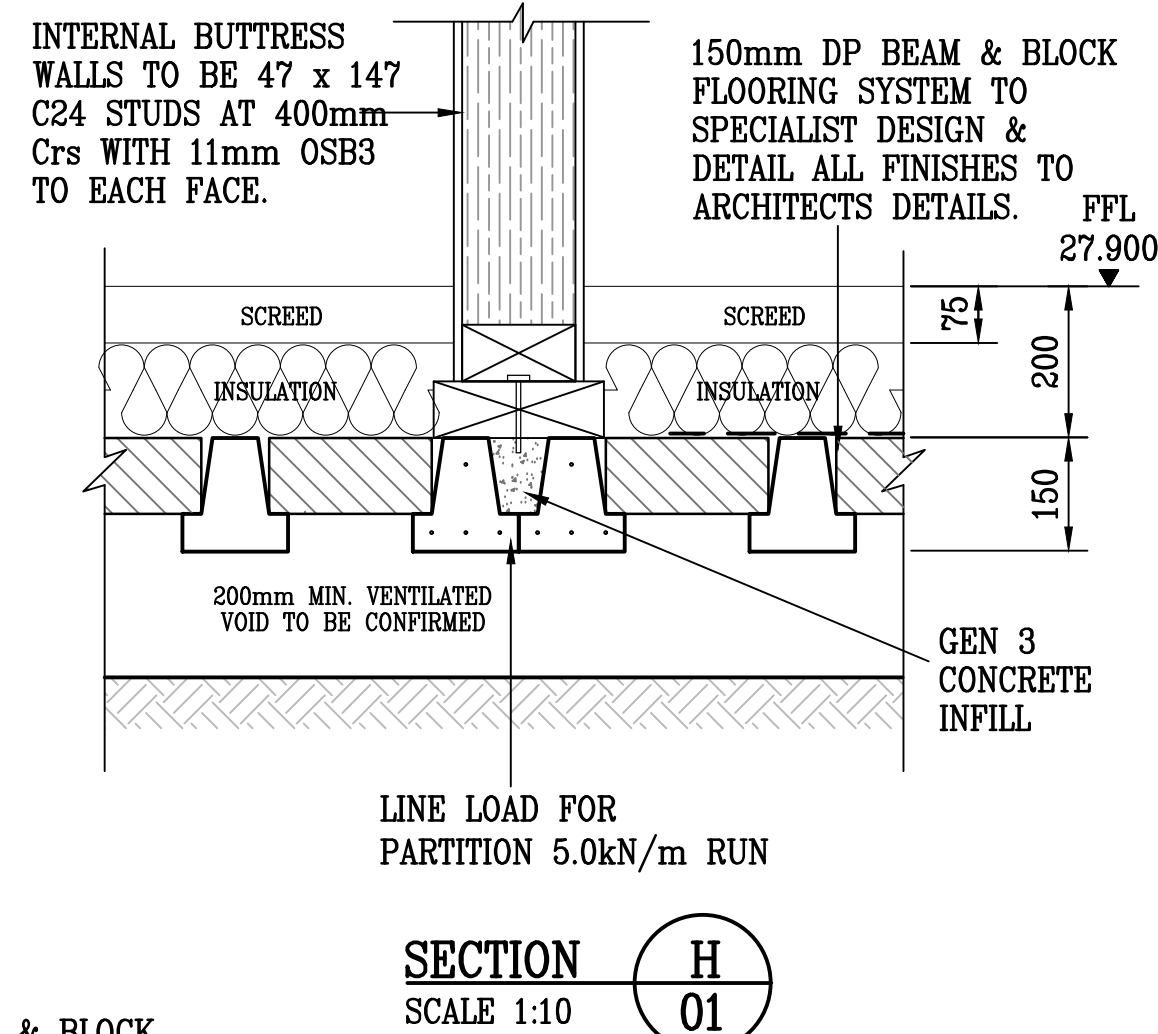
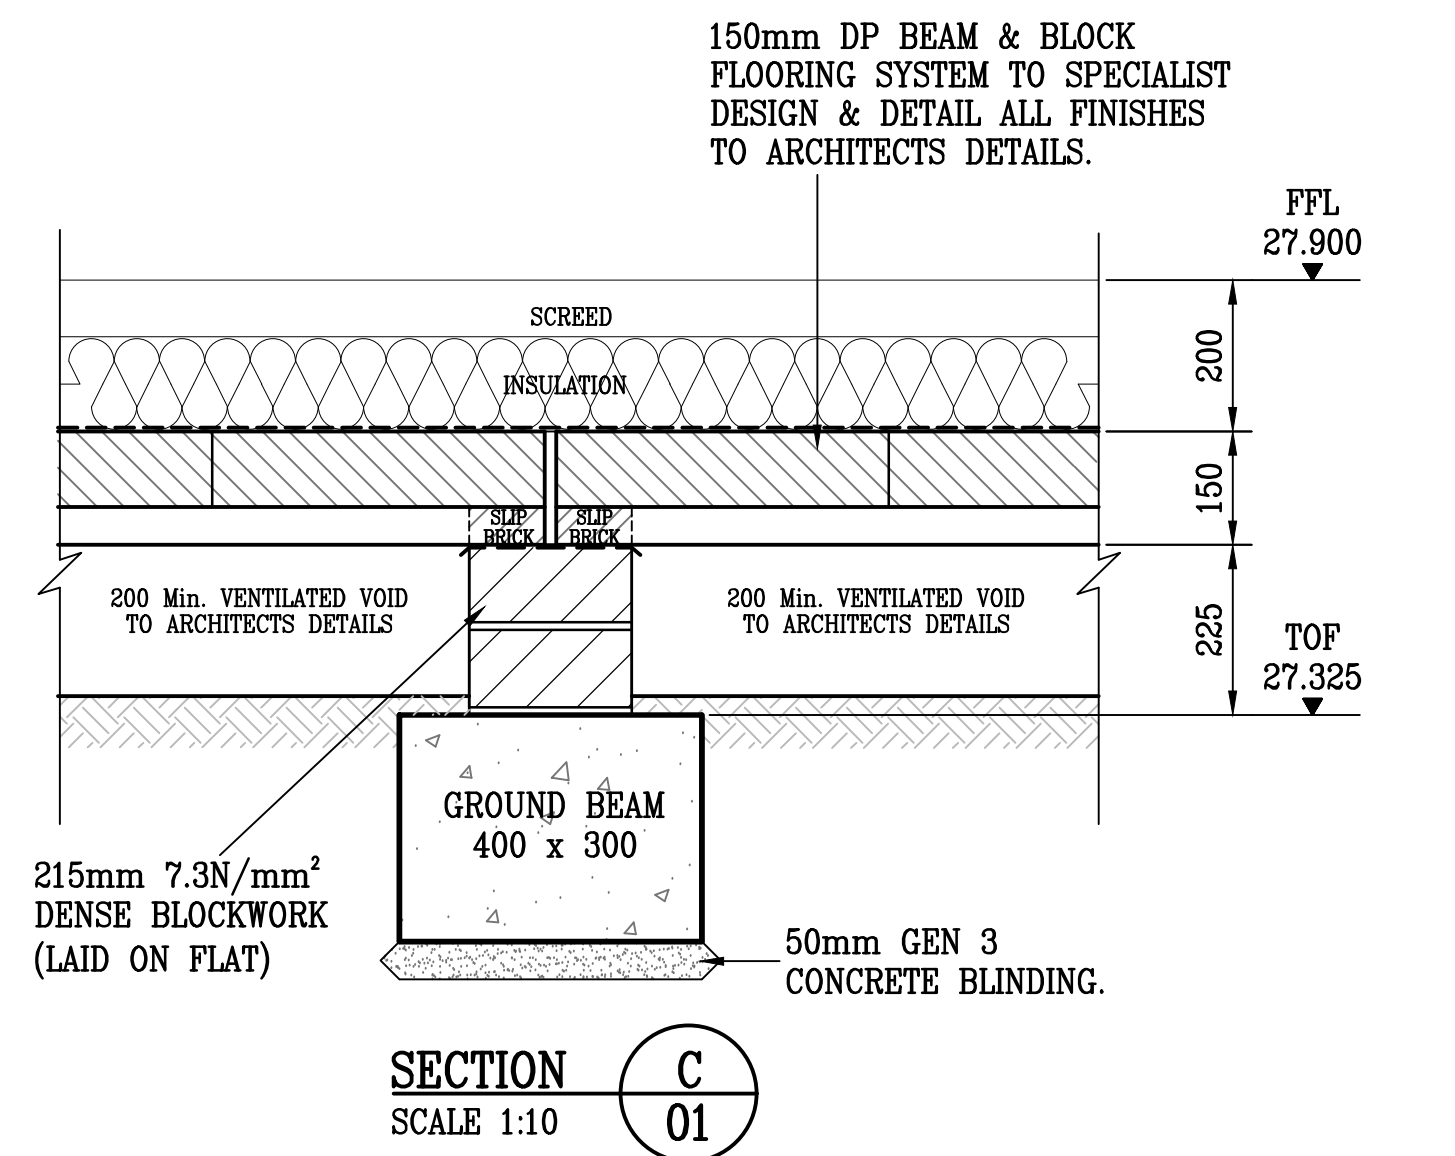
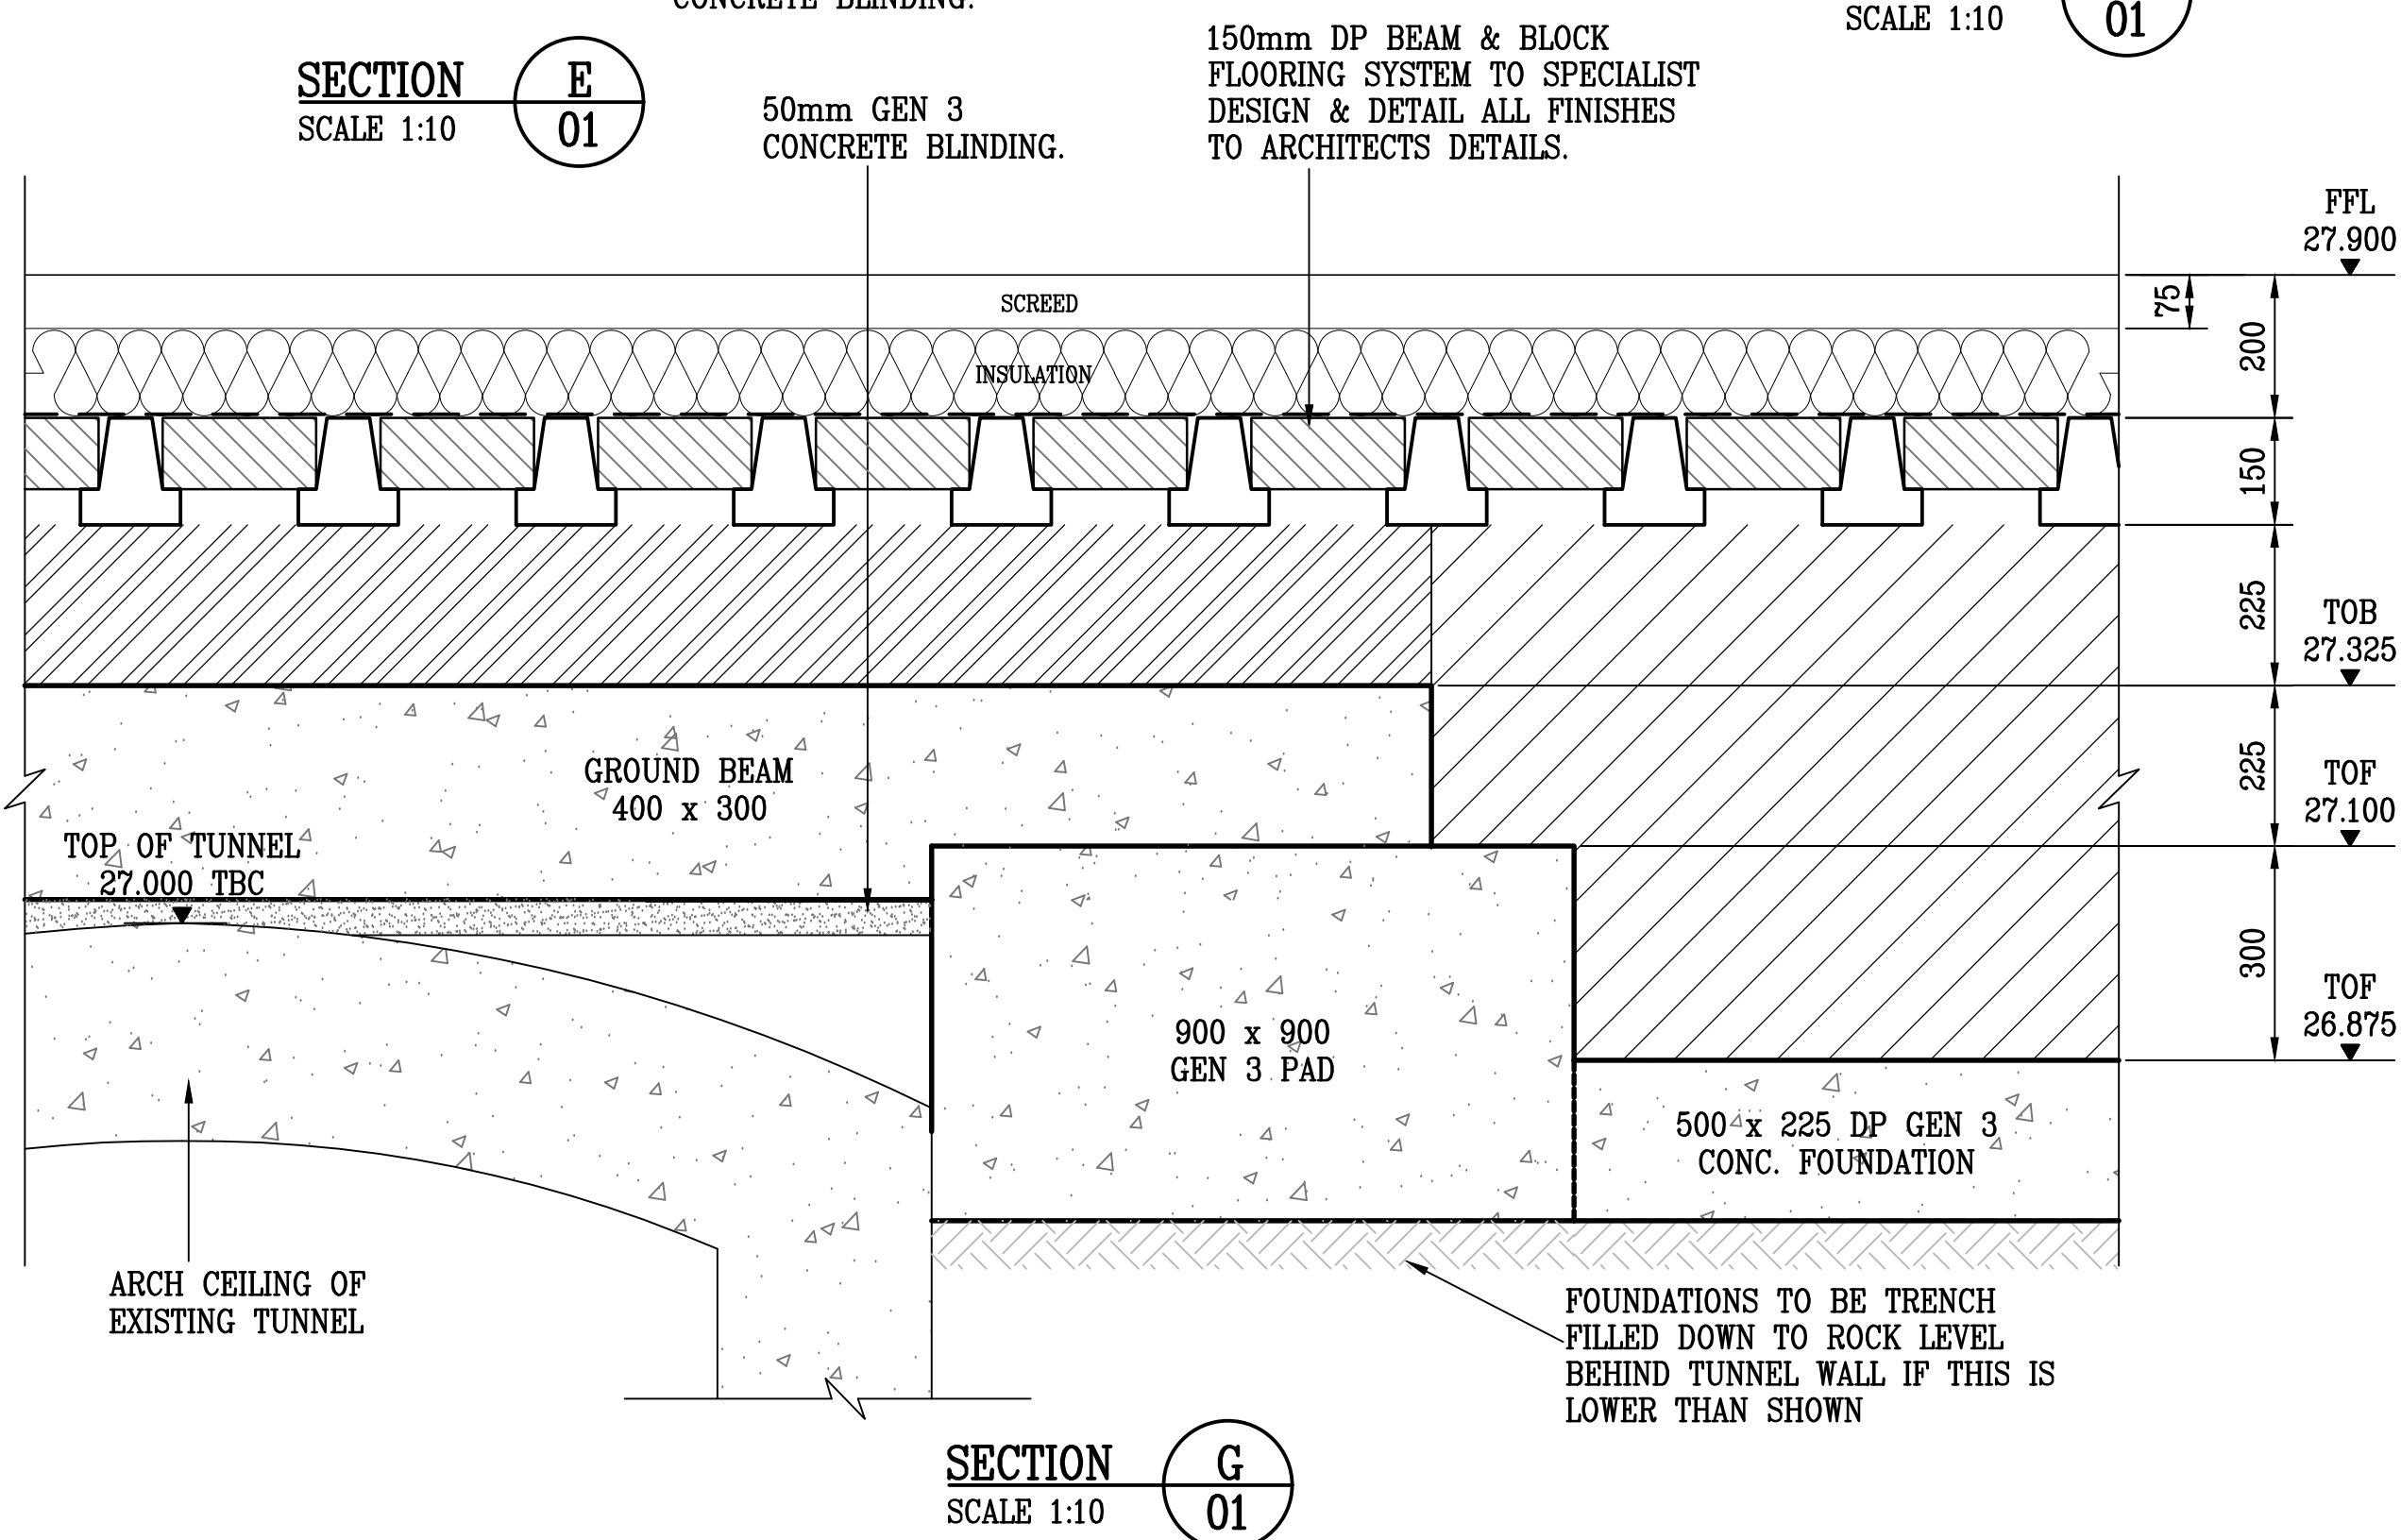
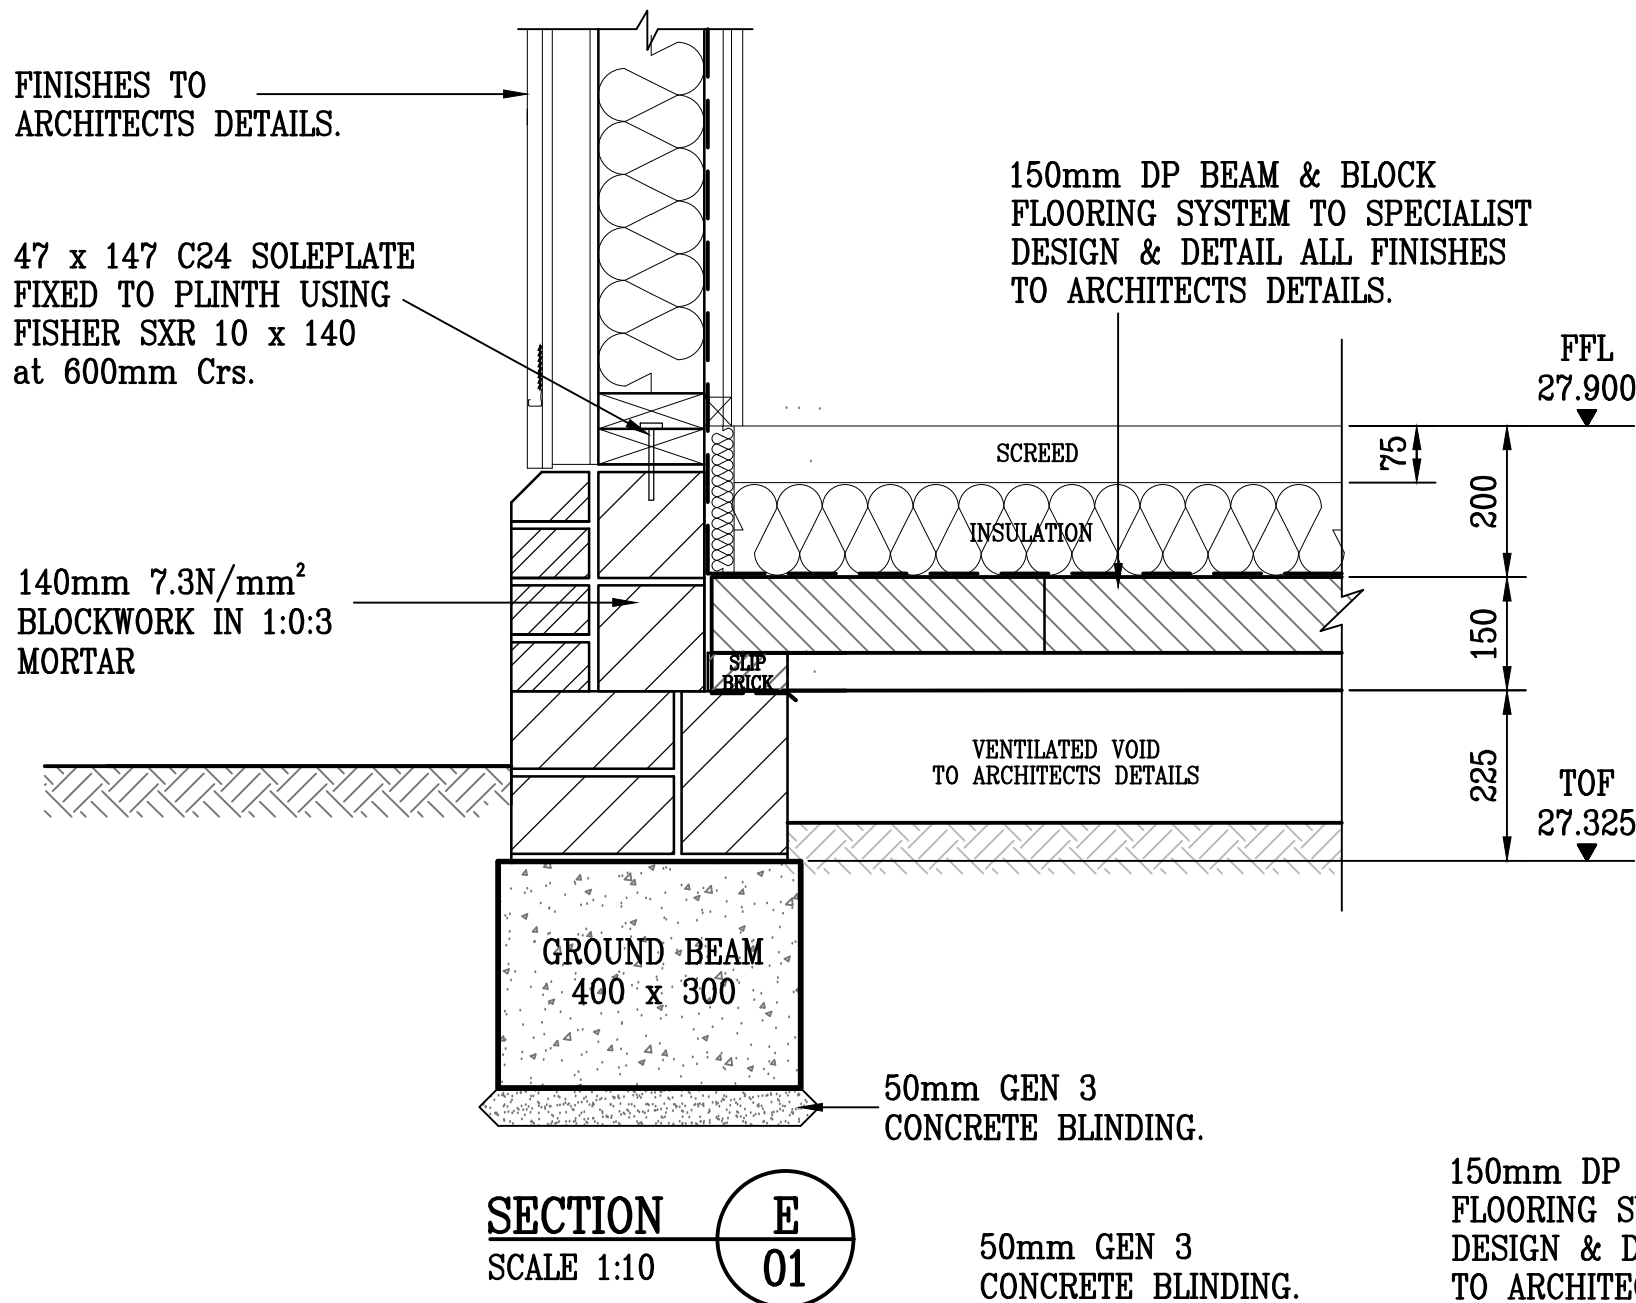
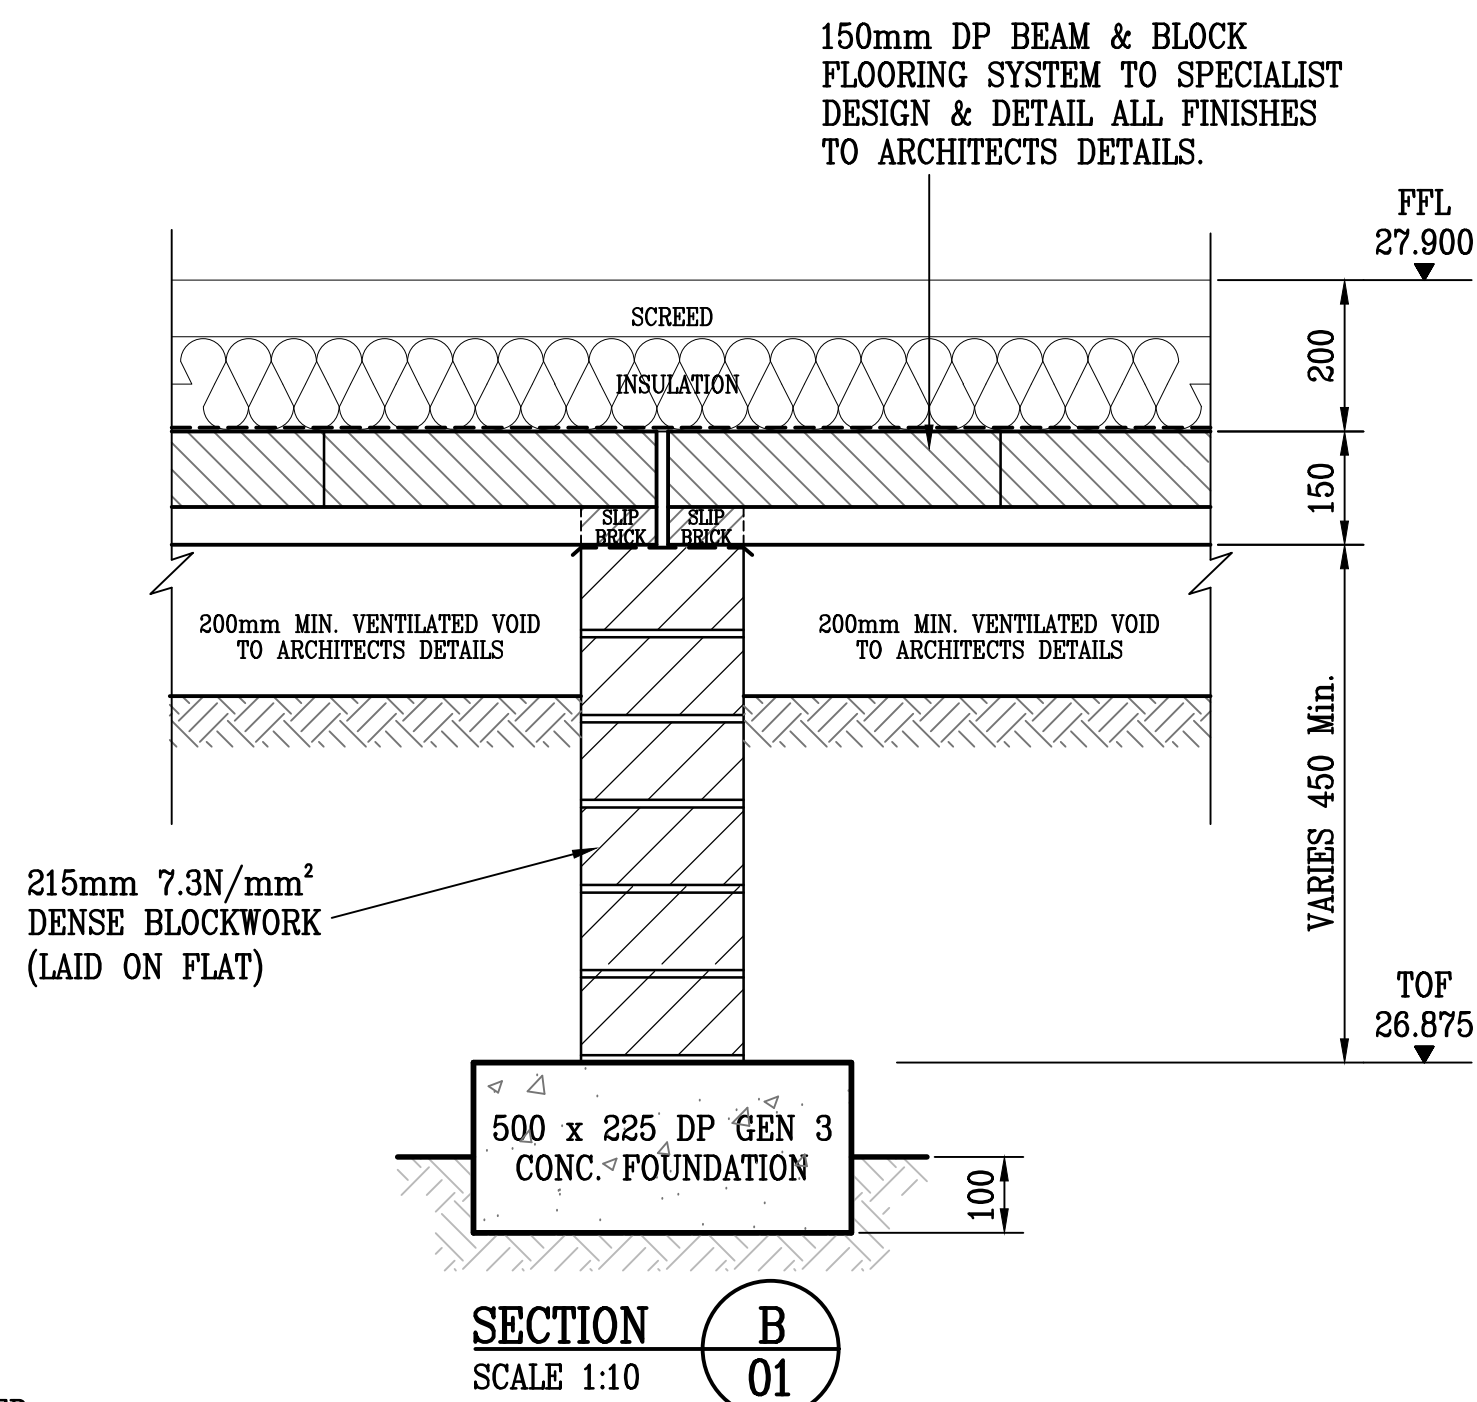
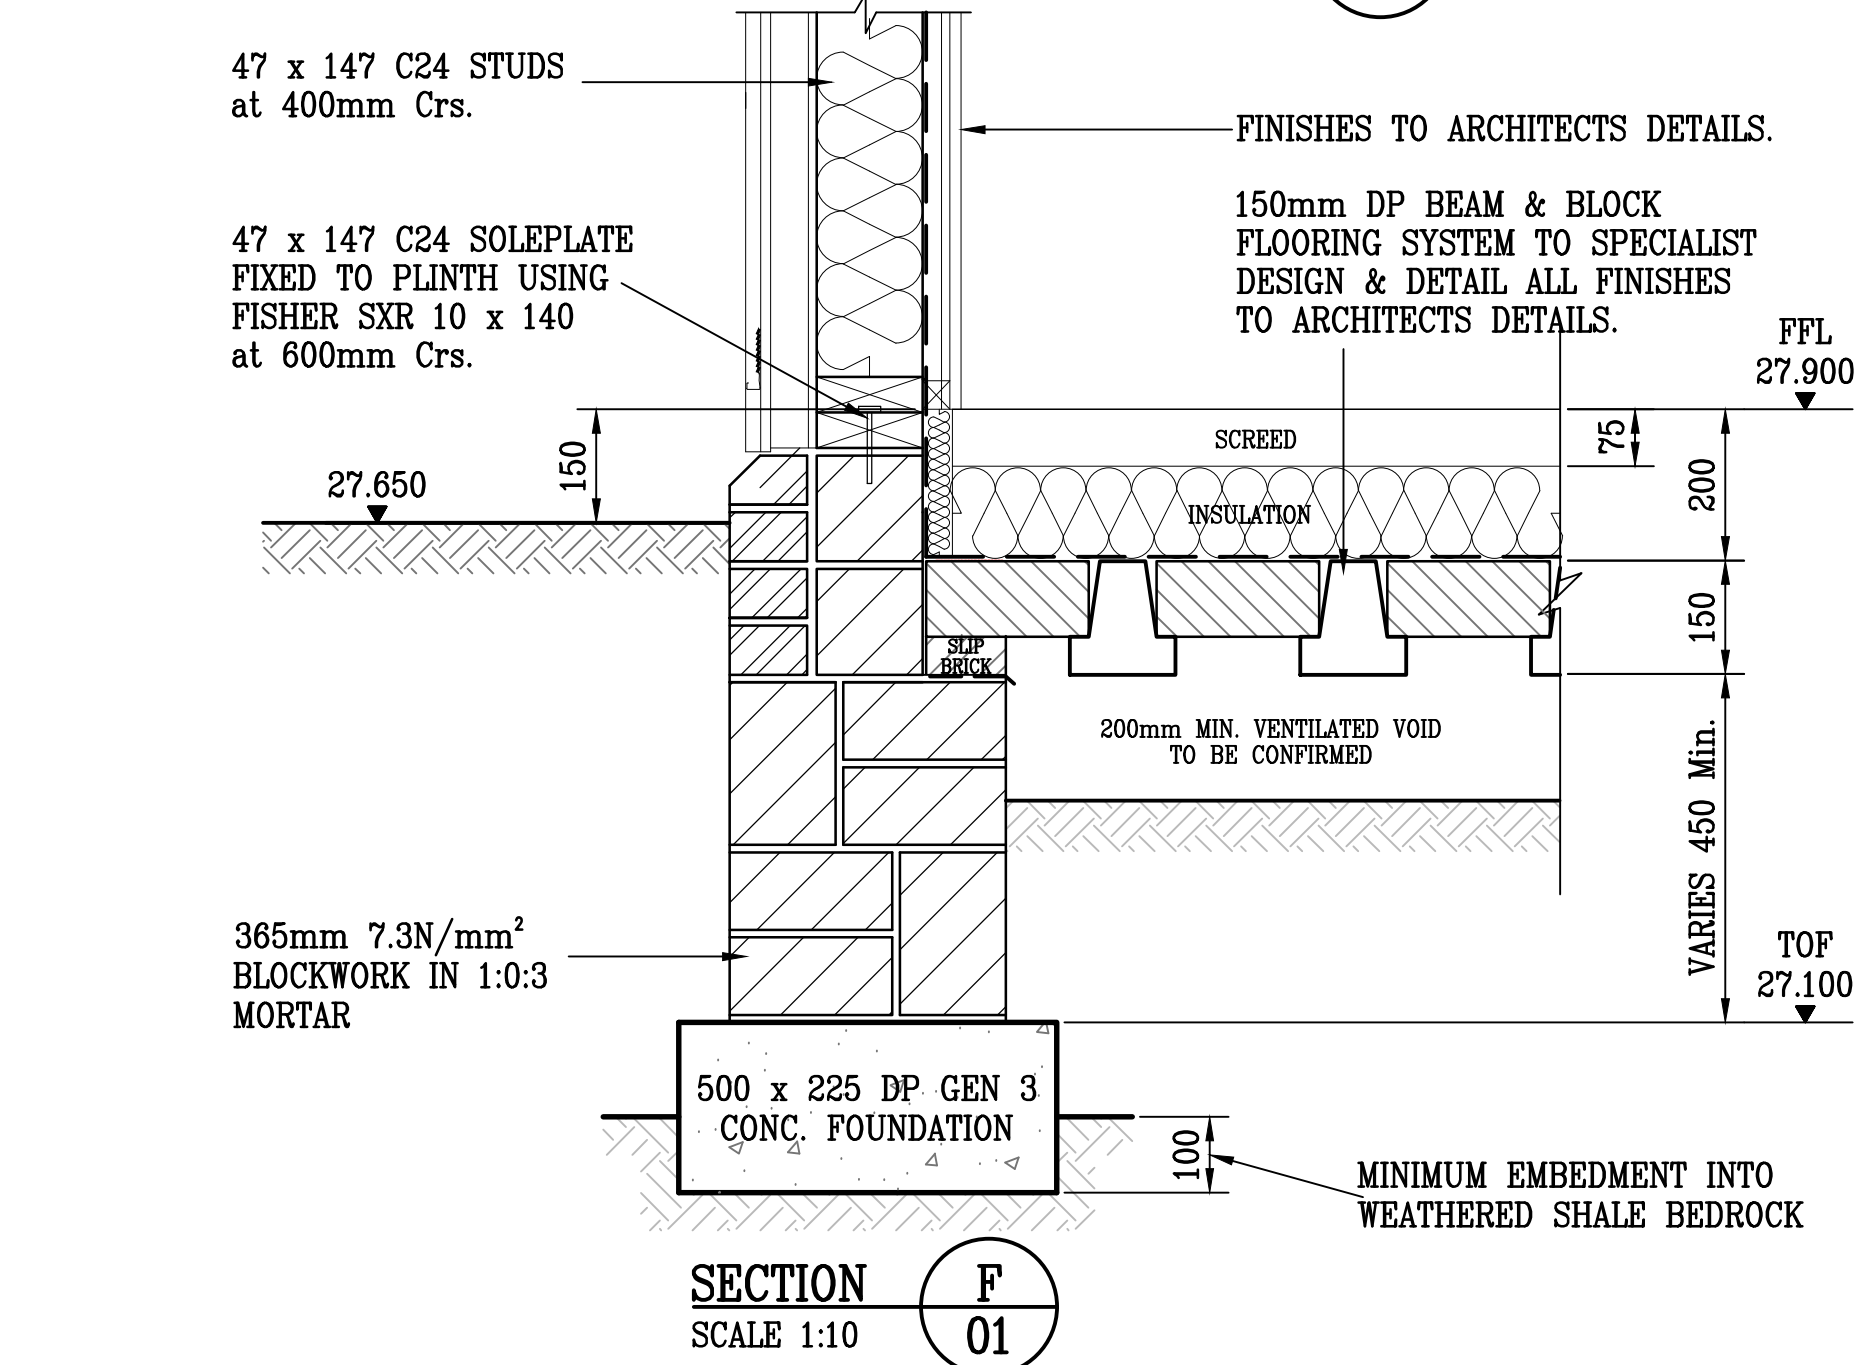
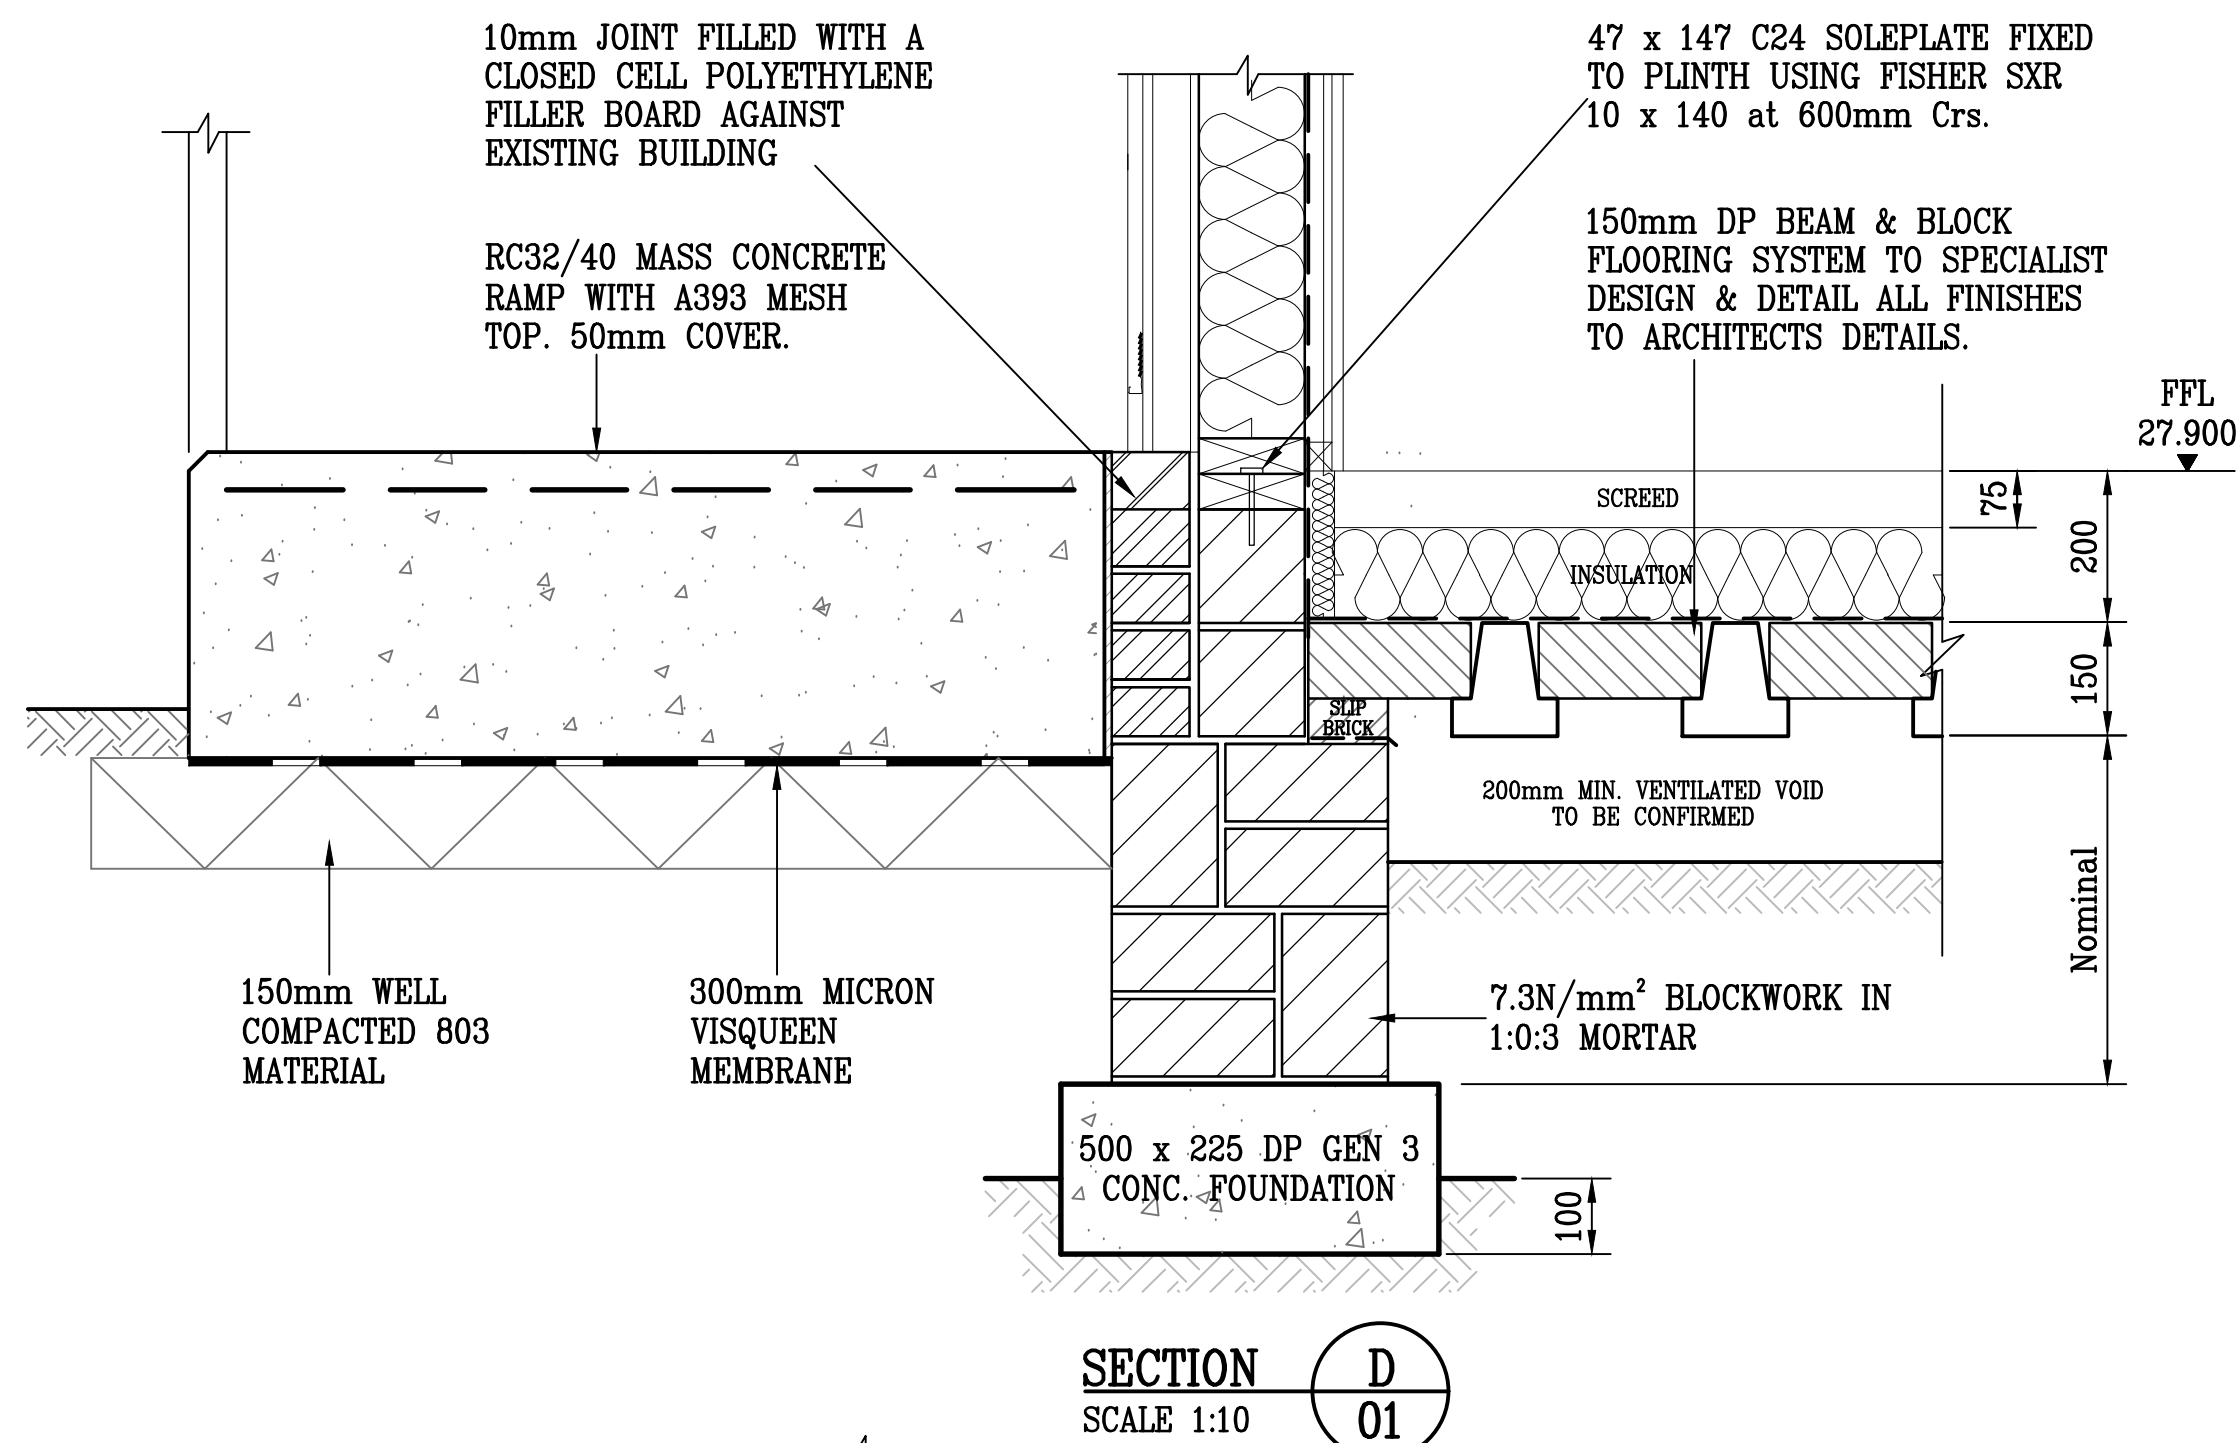


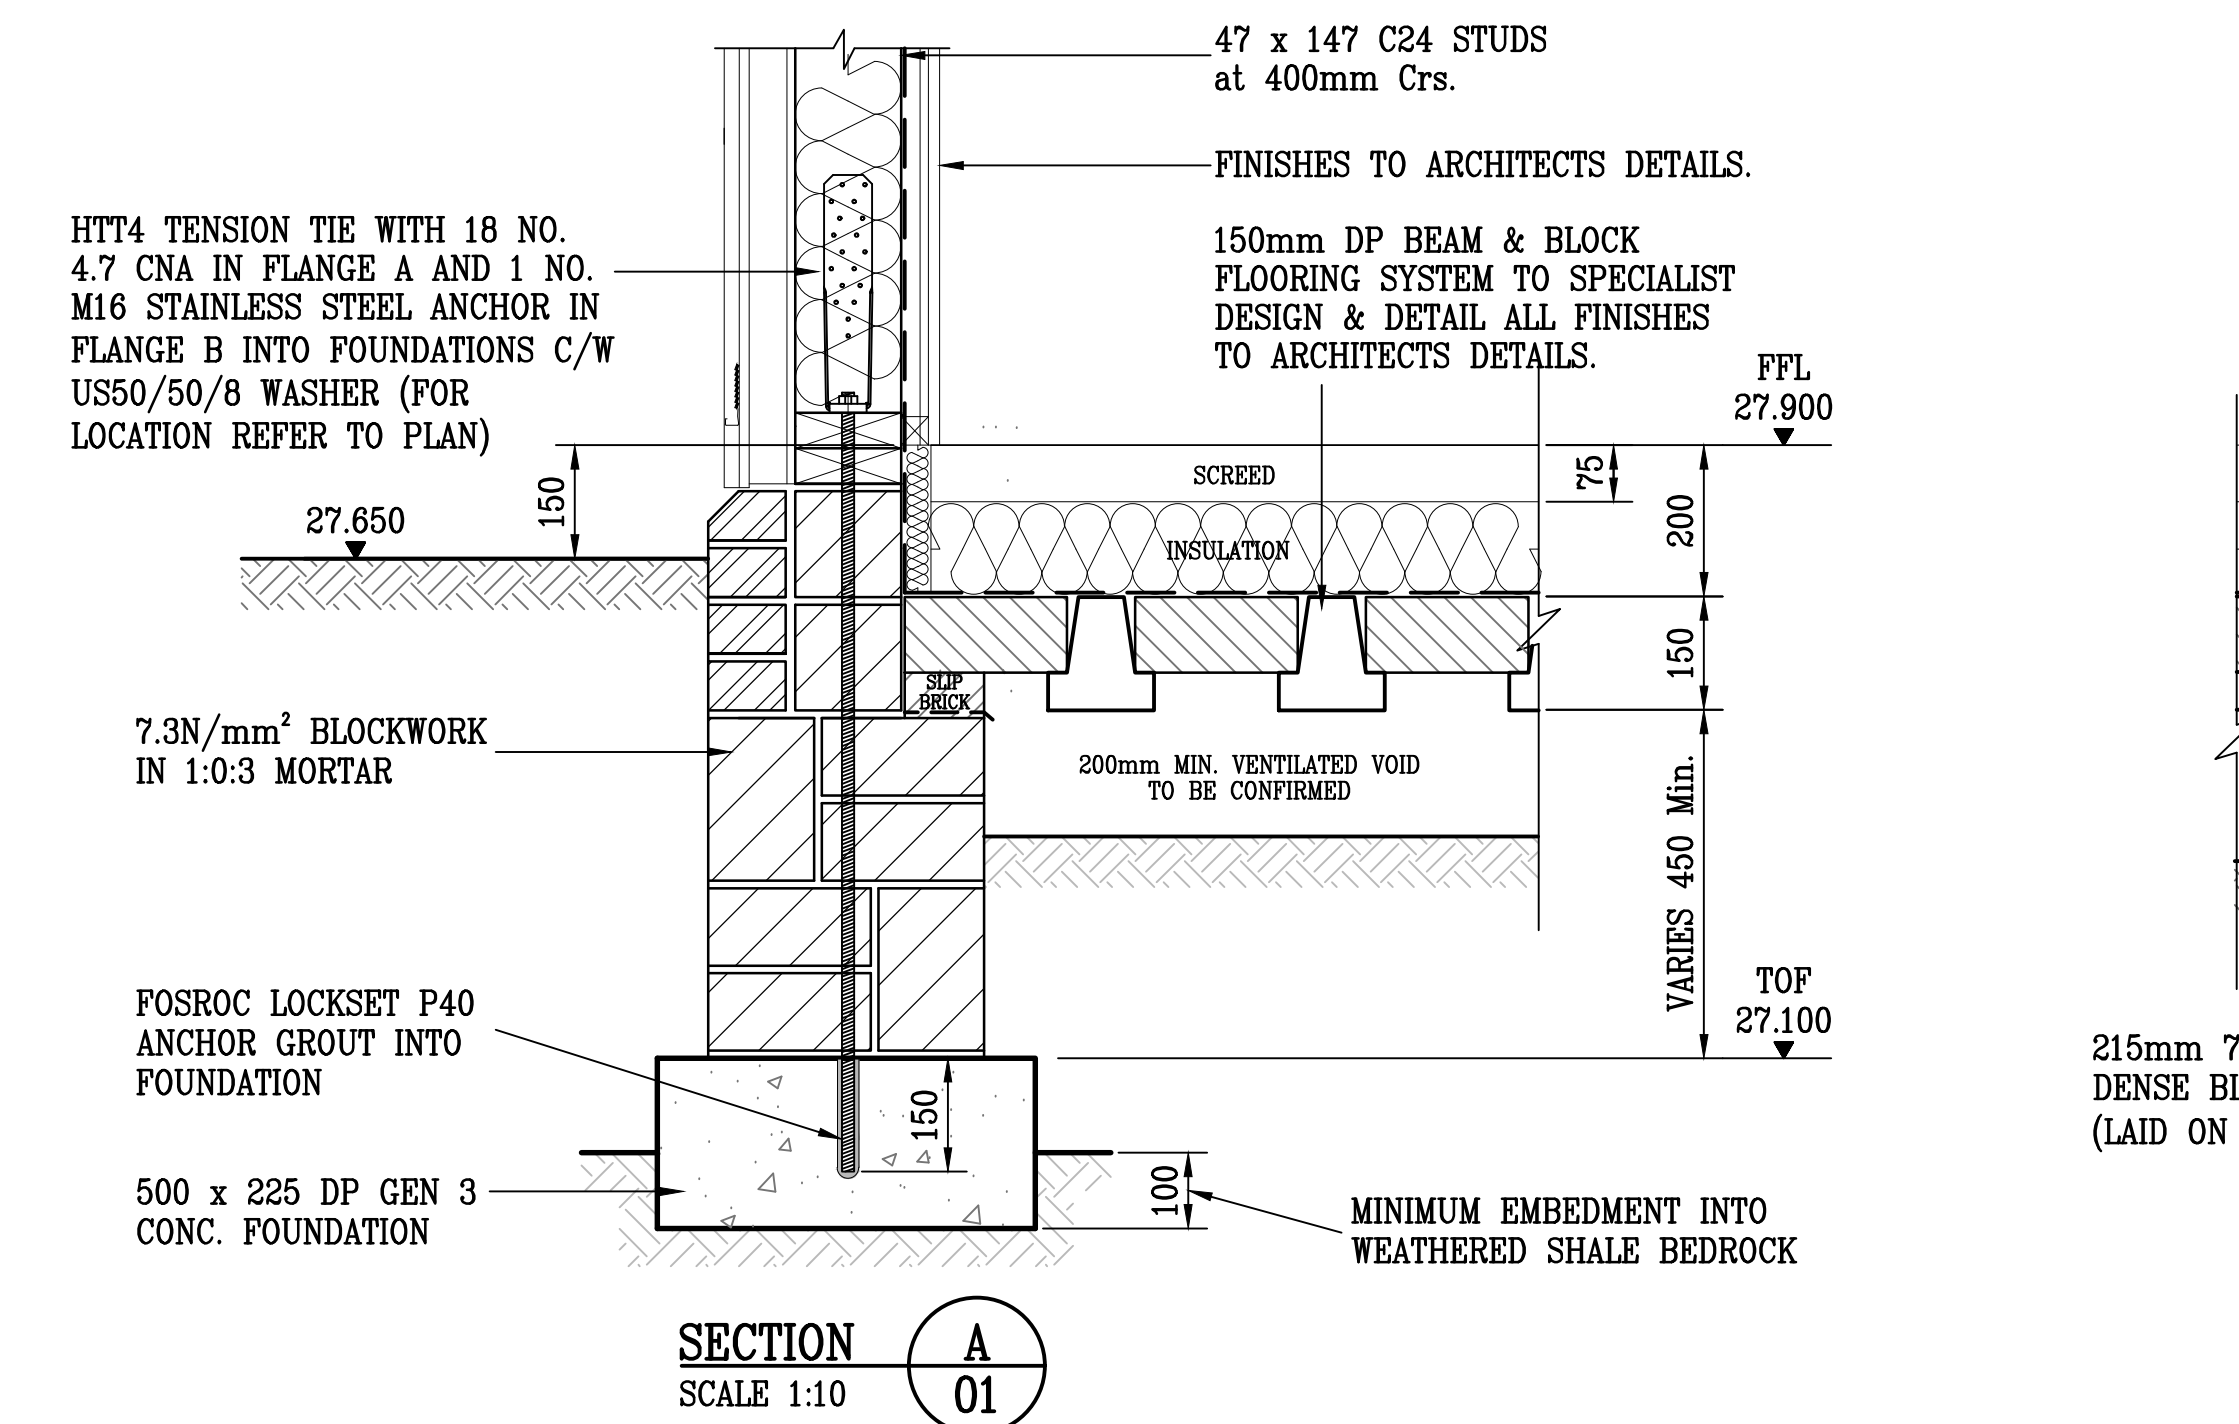

THIS DRAWING IS COPYRIGHT CASE CONSULTANTS. CONTRACTORS MUST CHECK ALL DIMENSIONS ON SITE ONLY FIGURED DIMENSIONS ARE TO BE WORKED FROM. DISCREPANCIES MUST BE REPORTED IMMEDIATELY TO THE ENGINEER BEFORE PROCEEDING

Notes.

- THIS DRAWING TO BE READ IN CONJUNCTION WITH ALL RELEVANT ARCHITECTS AND ENGINEERS DRAWINGS.
- ALL DIMENSIONS AND LEVELS TO BE CHECKED BY CONTRACTOR PRIOR TO COMMENCEMENT OF WORKS.
- ALL CONCRETE WORKS TO COMPLY WITH BS EN 1992: EUROCODE 2: DESIGN OF CONCRETE STRUCTURES.
- ALL MASONRY WORKS TO COMPLY WITH BS EN 1996: EUROCODE 6: DESIGN OF MASONRY STRUCTURES.
- ALL FOUNDATION EXCAVATIONS TO BE INSPECTED BY LOCAL AUTHORITY PRIOR TO CONCRETE PLACEMENT.

WORKS ON SITE MUST ONLY BE UNDERTAKEN FROM CONSTRUCTION STATUS DRAWINGS.

JOB

SALISBURY ROAD PRIMARY SCHOOL CLASSROOM REFURB

DETAIL

FOUNDATIONS AND GROUND FLOOR SECTIONS

CLIENT/ARCHITECT

MERCURY CONSTRUCTION BAILEY PARTNERSHIP

STATUS OF DRAWING

PRELIMINARY

DATE OF ISSUE

15 DECEMBER 2023

SCALE

1:10

PAPER SIZE

A1

DATE

NOV 2023

BY

D.P.H

DRAWING No.

C8765 / 02

REV

P1

CHECKED

CASE Consultants

Civil And Structural Engineers

Moose Hall
Barewell Road
Torquay
South Devon
TQ1 4PA
TEL : 01803 200175
E-mail : admin@caseconsultants.net
Website : www.caseconsultants.net

CASE Consultants is a trading name of C & A Consultants (Torquay) Limited, Registered in England & Wales Registration No. 02773632. Registered Office: Tor Hill House, Union Street, Torquay, TQ2 5W. CASE Consultants is a subsidiary of Torbay Economic Development Company Ltd.