




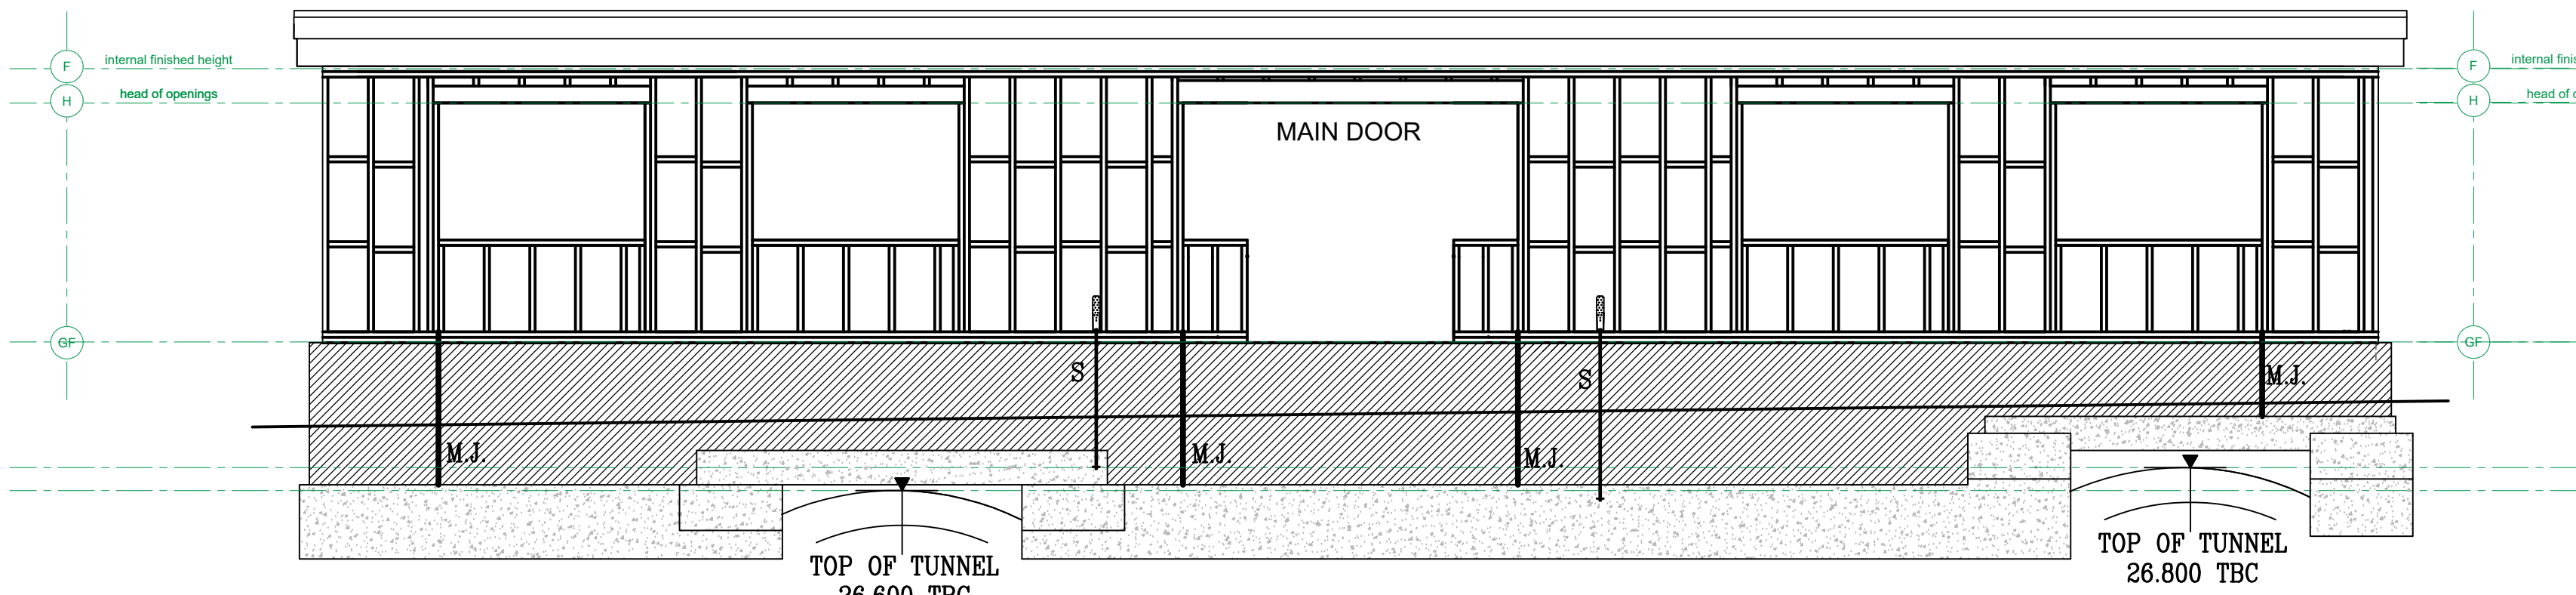


ELEVATION ON GRIDLINE C
SCALE 1:50

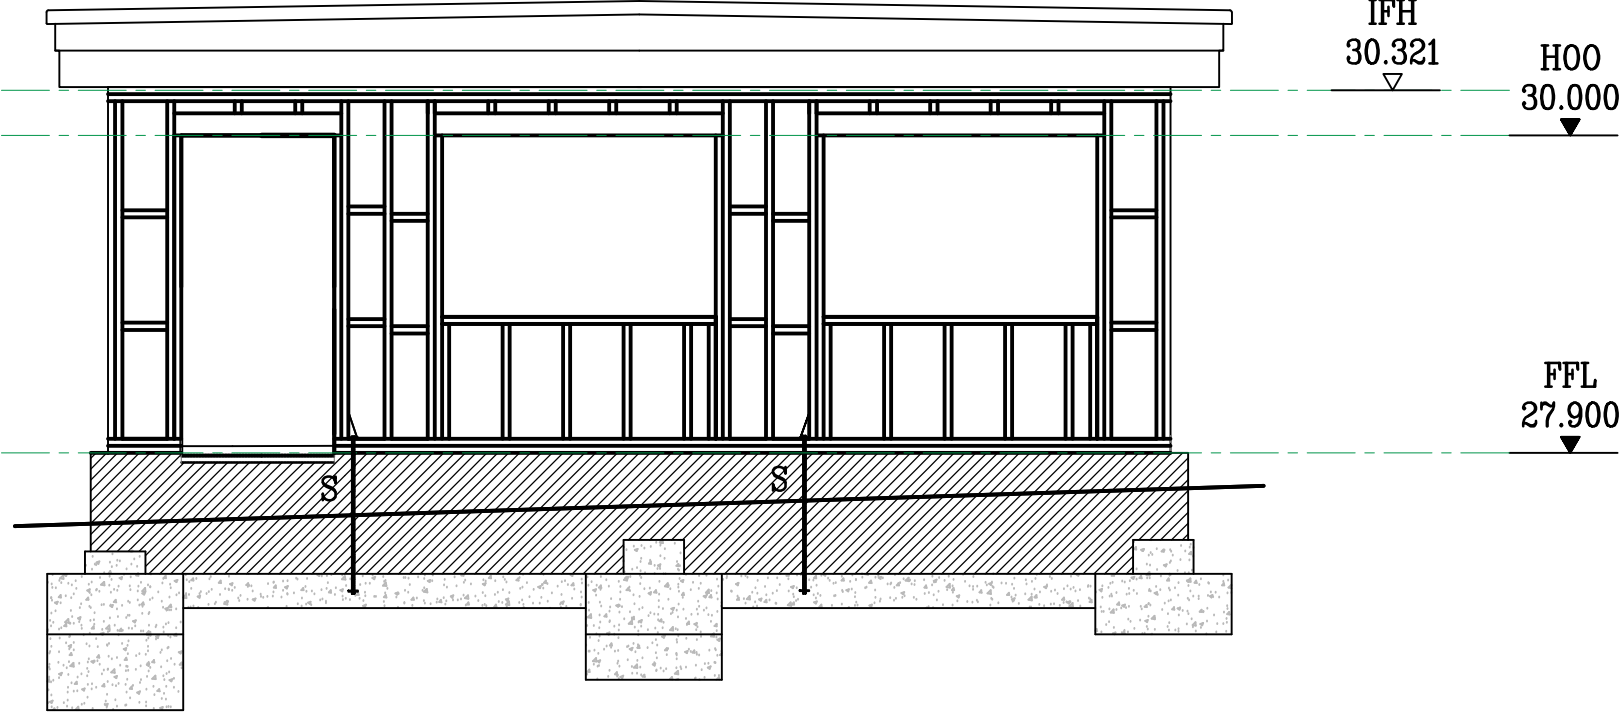


ELEVATION ON GRIDLINE 5
SCALE 1:50

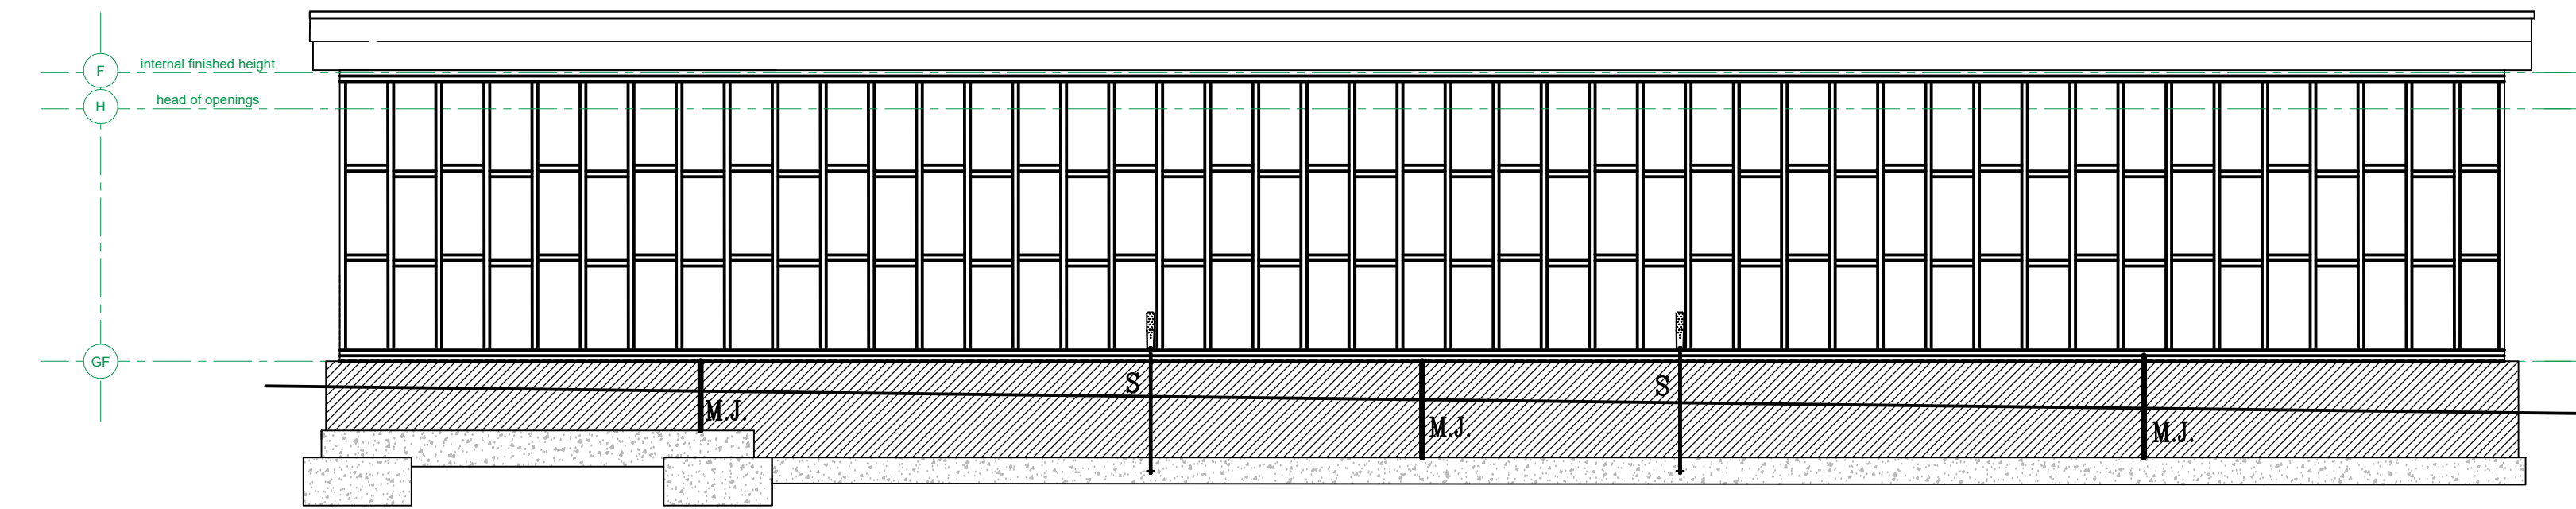

ELEVATION ON GRIDLINE A
SCALE 1:50

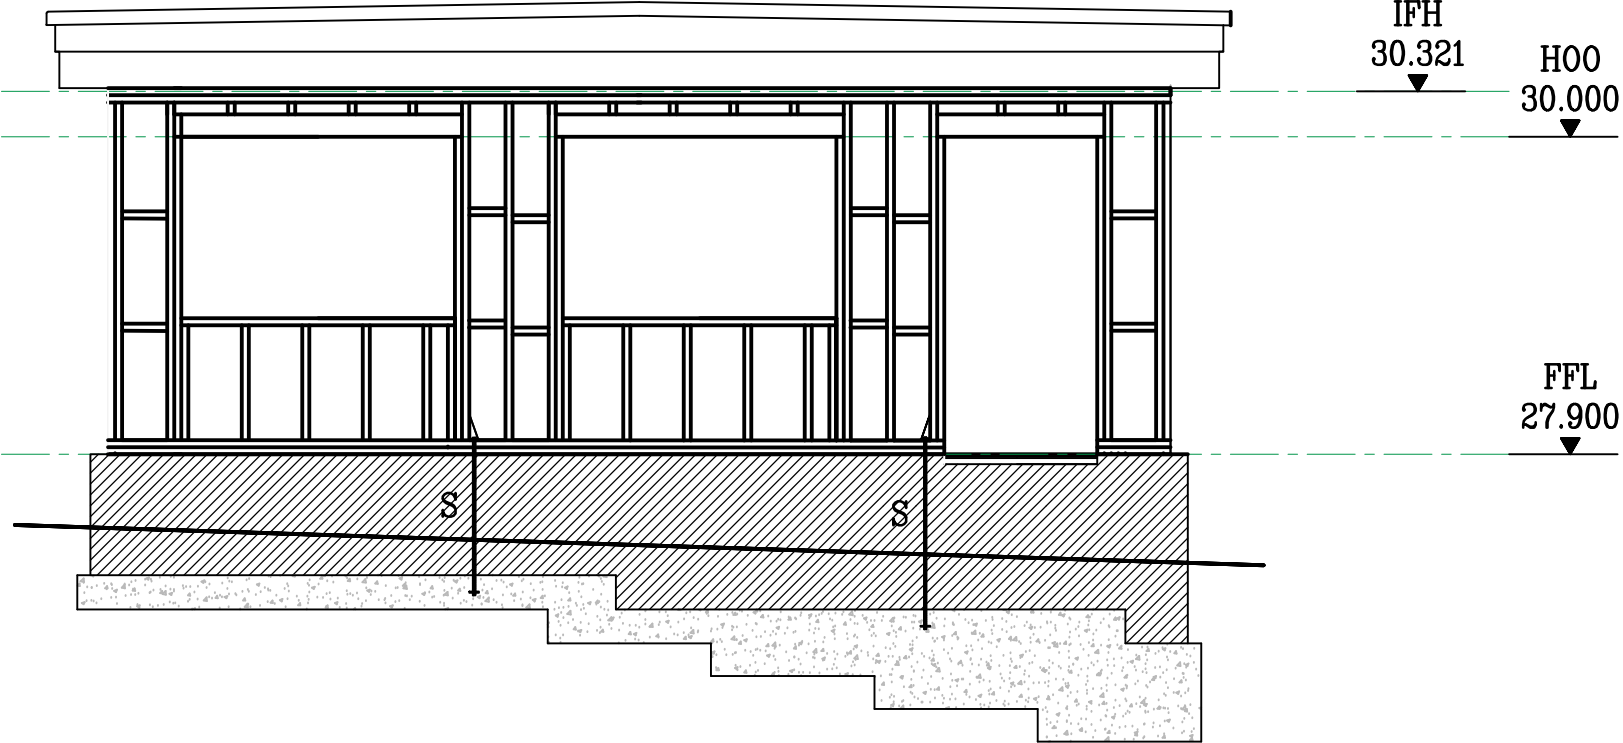

ELEVATION ON GRIDLINE 1
SCALE 1:50

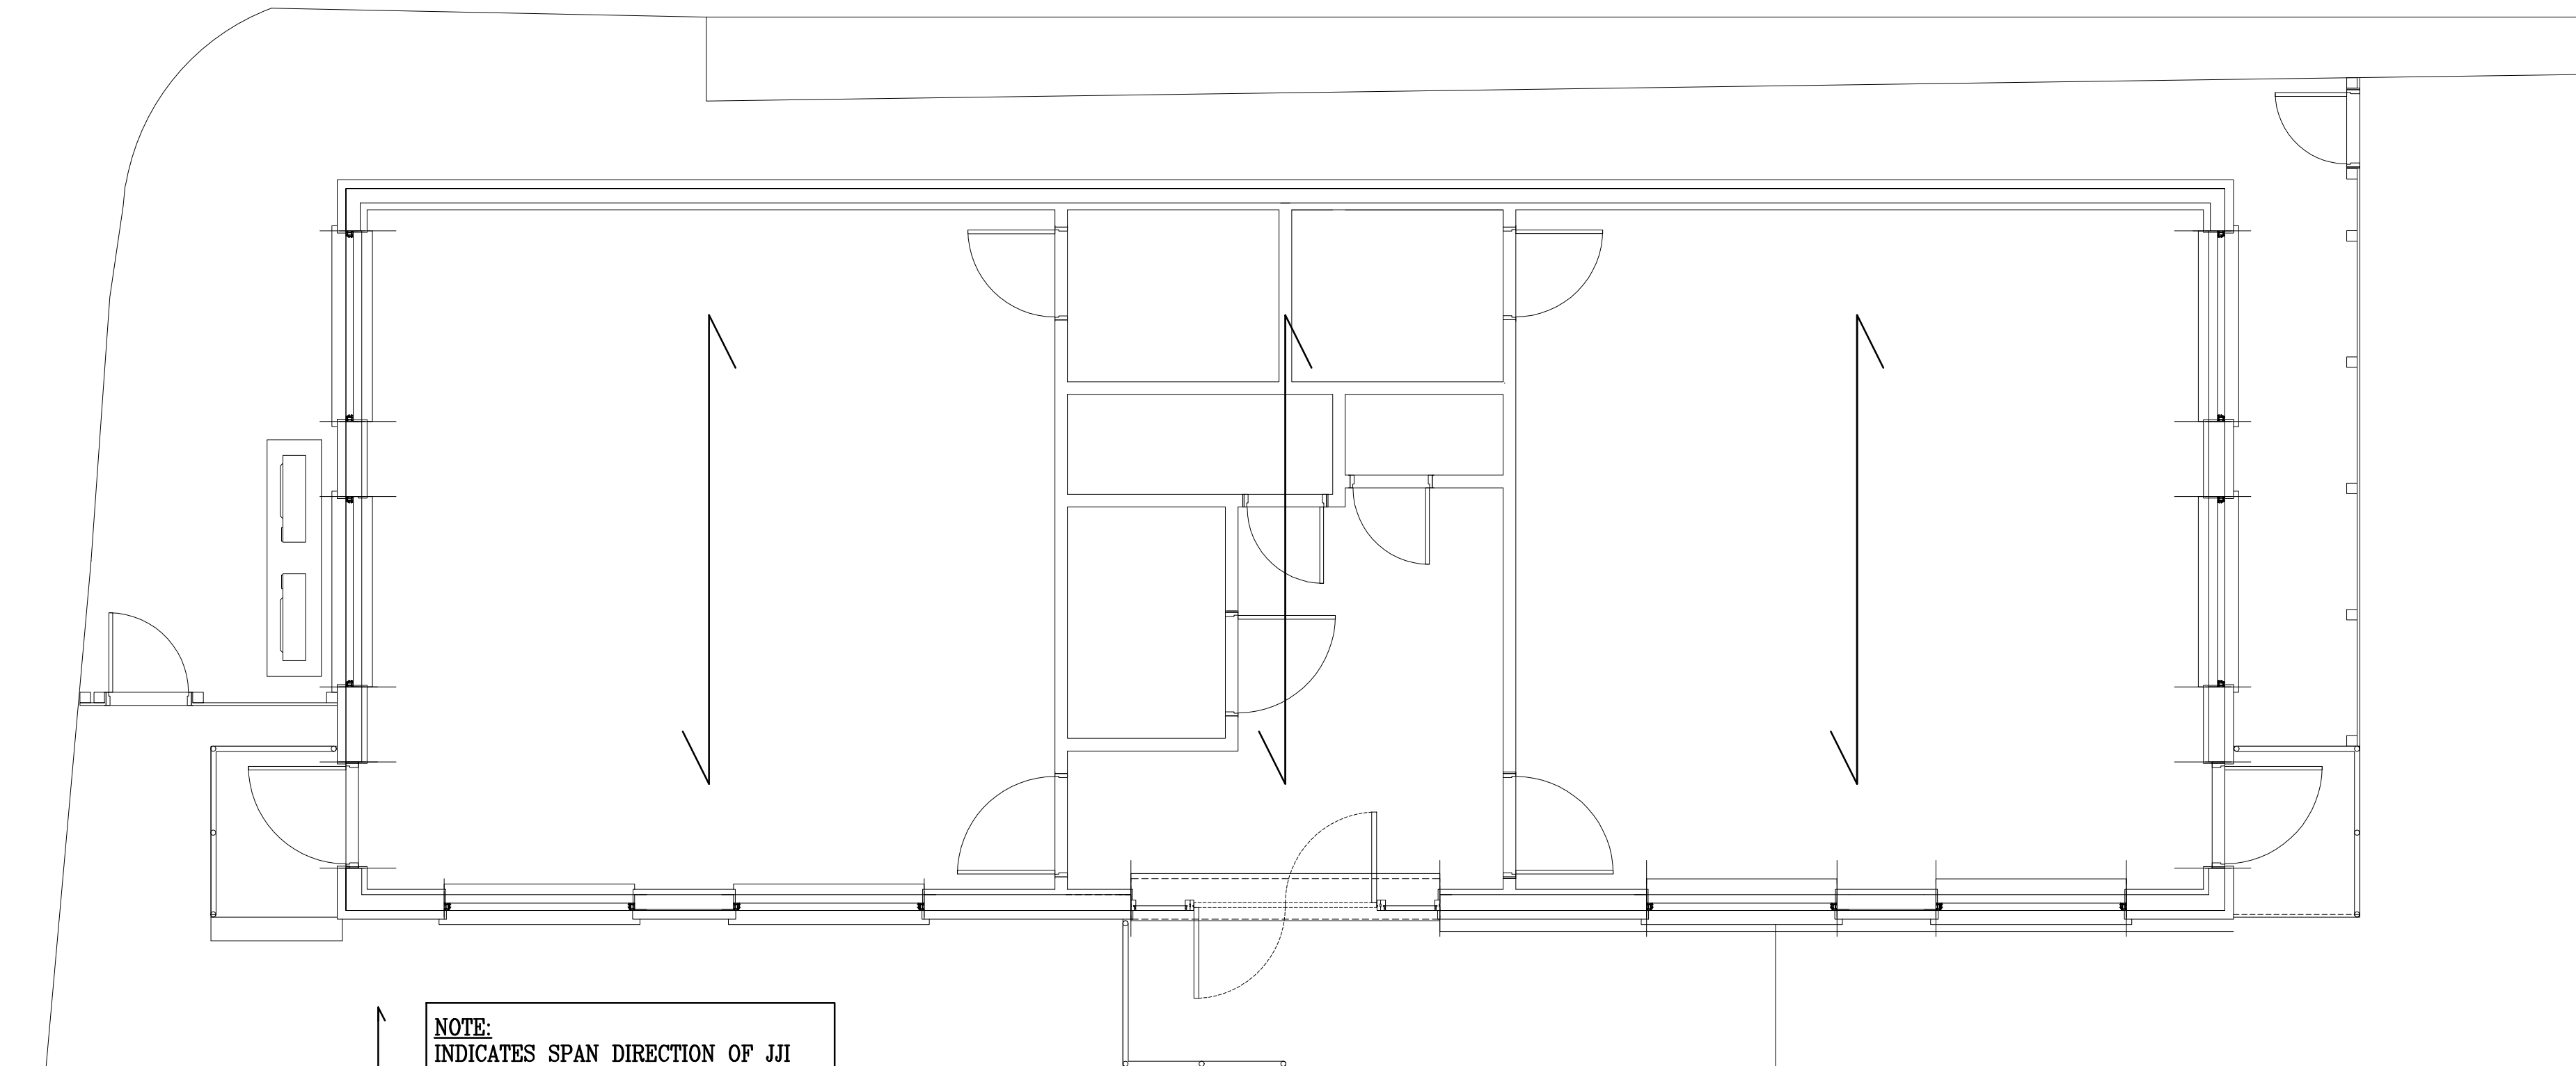

NOTE:
INDICATES SPAN DIRECTION OF JJ1
245 D JOISTS AT 400 CRS. TO BE
SUBJECT TO SPECIALIST
DESIGN FOR THE FOLLOWING LOADS:
DEAD LOADS = 0.75KN/m²
P.V. ALLOWANCE = 0.25KN/m²
LIVE LOAD = 0.60KN/m²

ROOF PLAN
SCALE 1:50

NOTE:
MOVEMENT JOINTS SHOWN IN BOLD
LINE (M.J.)

NOTE:
S INDICATES LOCATION OF SIMPSON
STRONGTIE HTT4 TENSION TIES
WITH M16 ANCHOR INTO
FOUNDATIONS

NOTE:
FOR DIMENSIONS REFER TO
ARCHITECTS GENERAL
ARRANGEMENT DRAWINGS

NOTE:
DOUBLE CRIPPLE STUD TO BE
USED ON ALL OPENINGS

NOTE:
WINDOW LINTELS TO BE 3 NO. 47 X
147 C24 WITH M12 GRADE 4.6
BOLTS @ 600 CENTERS C/W 36mm
X 3.0mm THICK WASHERS

NOTE:
MAIN DOOR LINTEL TO BE 3 NO. 47
X 195 C24 WITH M12 GRADE 4.6
BOLTS @ 600 CENTERS C/W 36mm
X 3.0mm THICK WASHERS

NOTE:
USE NOGGINGS AT THIRD HEIGHTS
WHERE OPENINGS ARE NOT
PRESENT

NOTE:
ALL STUDS TO BE 47 X 147 C24 @
400 CENTERS WITH 11 MM THICK
OSB/3 SHEATHING USING 3.1mm X
50mm NAILS @ 150 MAX CENTERS.

THIS DRAWING IS COPYRIGHT
CONTRACTORS MUST CHECK
ALL DIMENSIONS ON SITE
ONLY FIGURED DIMENSIONS
ARE TO BE WORKED FROM.
DISCREPANCIES MUST BE
REPORTED IMMEDIATELY TO
THE ENGINEER BEFORE
PROCEEDING

0m 1m 2m
1:50

Notes.

1. THIS DRAWING IS TO BE READ IN CONJUNCTION
WITH ALL RELEVANT ARCHITECTS AND ENGINEERS
DRAWINGS.

2. ALL DIMENSIONS AND LEVELS TO BE CHECKED
BY CONTRACTOR PRIOR TO COMMENCEMENT OF
WORKS.

3. ALL TIMBER WORKS TO COMPLY WITH
BS EN 1992: EUROCODE 5: DESIGN OF TIMBER
STRUCTURES.

REV	DATE	DESCRIPTION	BY
-----	------	-------------	----

WORKS ON SITE MUST ONLY BE UNDERTAKEN FROM CONSTRUCTION STATUS DRAWINGS.

JOB

**SALISBURY ROAD
PRIMARY SCHOOL**

DETAIL

**TIMBER FRAME
GENERAL ARRANGEMENT**

CLIENT/ARCHITECT

**MERCURY CONSTRUCTION
ROGERS AND JONES**

STATUS OF DRAWING

PRELIMINARY 15 DECEMBER 2023

SCALE	PAPER SIZE	DATE	BY
1:50	A1	DEC 2002	D.P.H

DRAWING No.	REV	CHECKED
C8765 / 03	P	



CASE Consultants
Civil And Structural Engineers

Moose Hall
Barewell Road
Torquay
South Devon
TQ1 4PA
TEL : 01803 200175

E-mail : admin@caseconsultants.net
Website : www.caseconsultants.net

CASE Consultants is a trading name of C & A Consultants (Torquay) Limited,
Registered in England & Wales Registration No. 02773632.
Registered Office: Tor Hill House, Union Street, Torquay, TQ2 5W.
CASE Consultants is a subsidiary of Torbay Economic Development Company Ltd.