
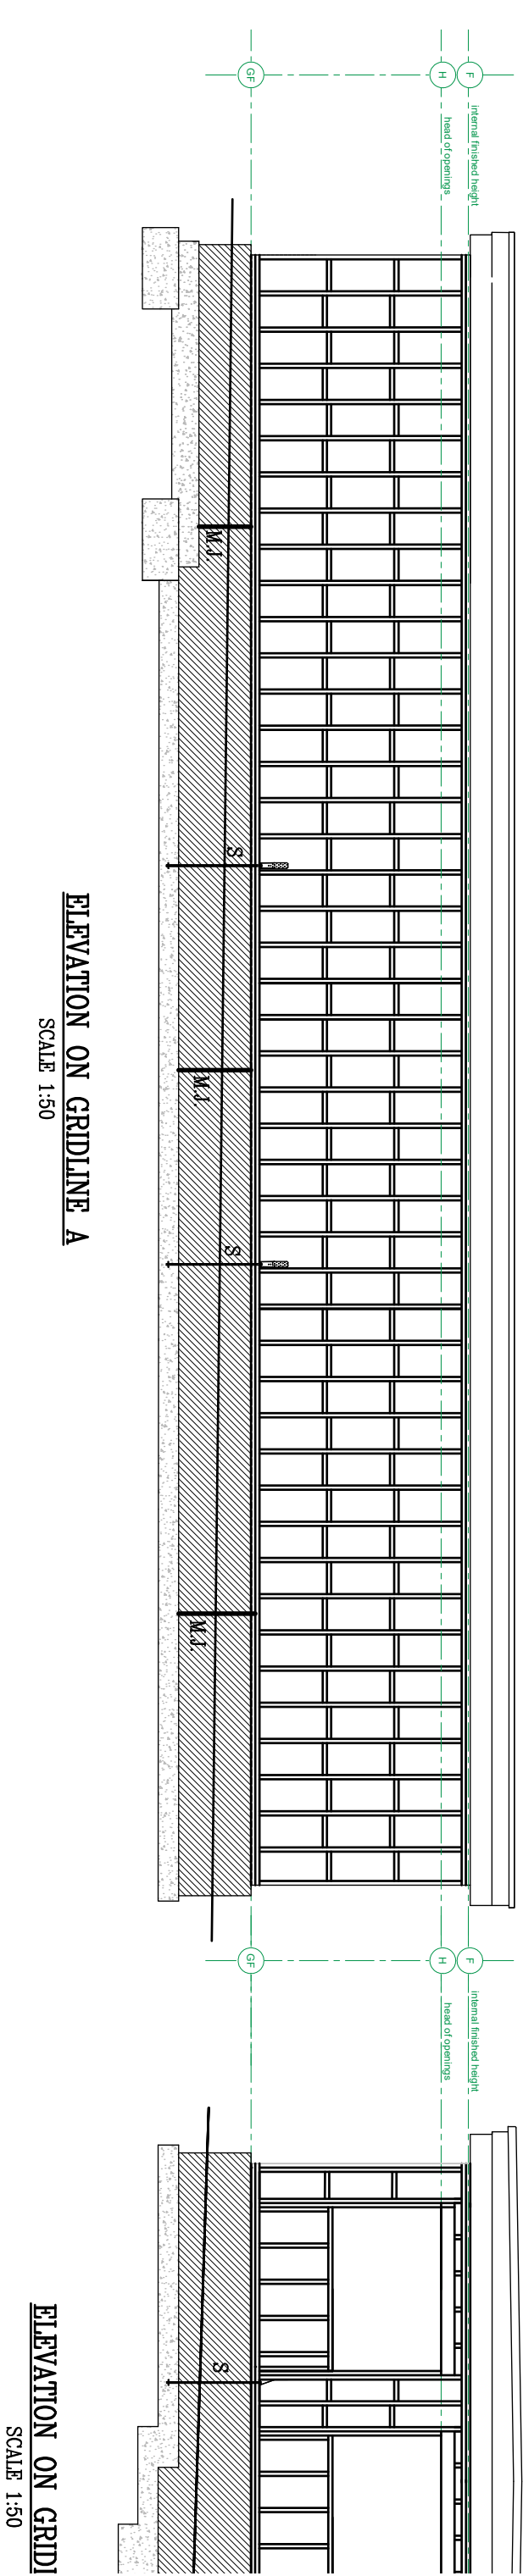


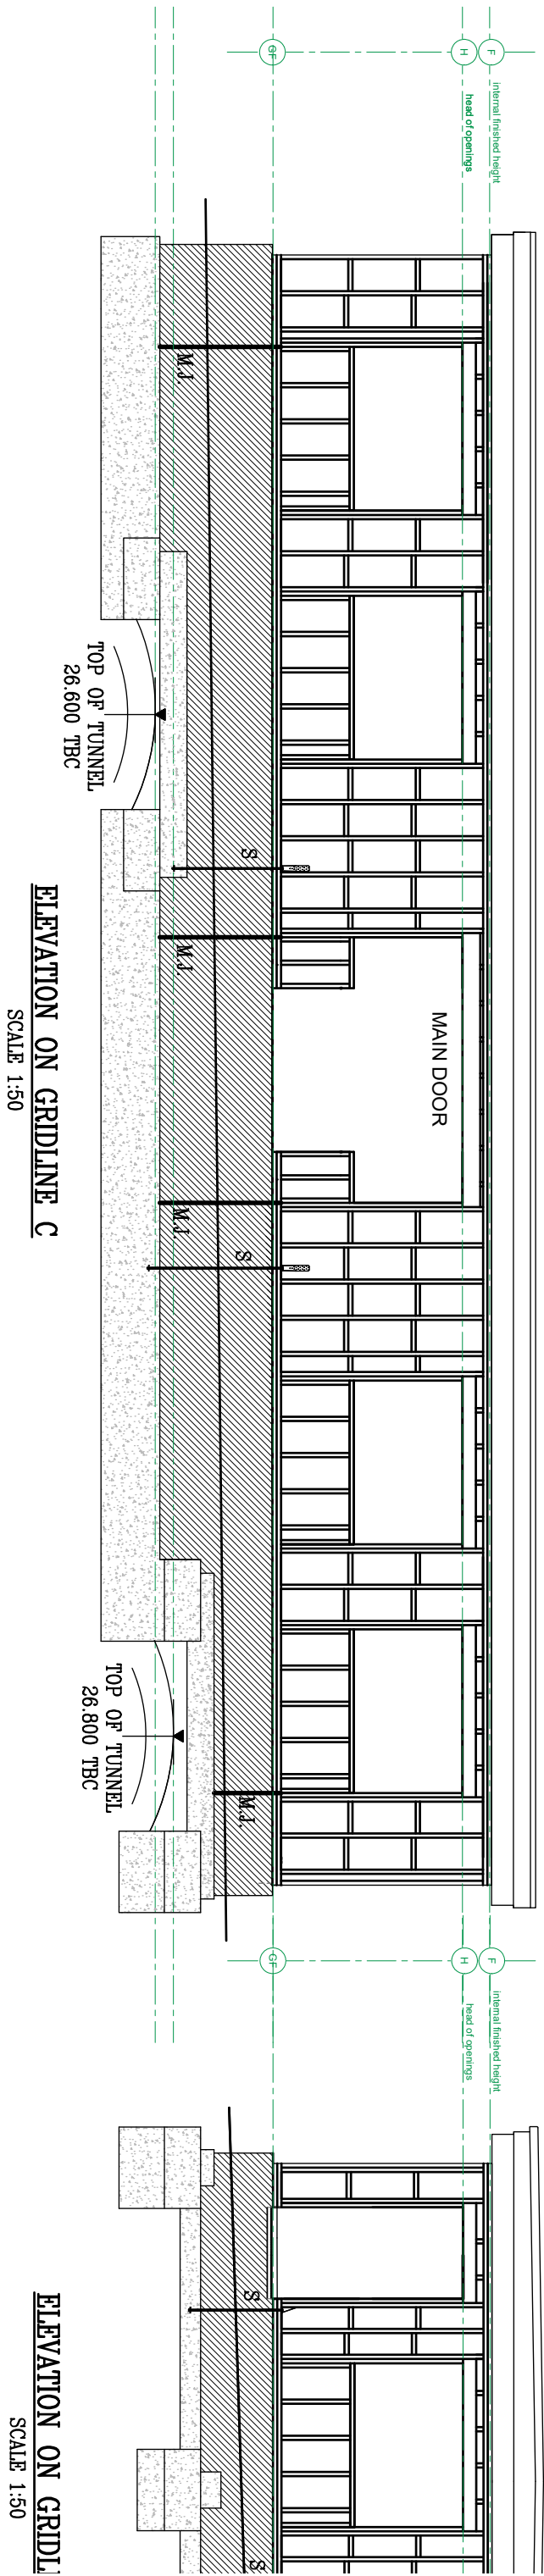

NOTE:
MOVEMENT JOINTS SHOWN IN
LINE (M.J.)

NOTE:
FOR DIMENSIONS REFER TO
ARCHITECT'S GENERAL
ARRANGEMENT DRAWINGS

NOTE:
WINDOW LINTELS TO BE 3 NO
4FT C24 WITH M12 GRID/ 4.C
1200 X 3000 X 3/8" THICK WASHERS

NOTE:
USE NOGGINGS AT THIRD HE
WHERE OPENINGS ARE NOT
PRESENT

